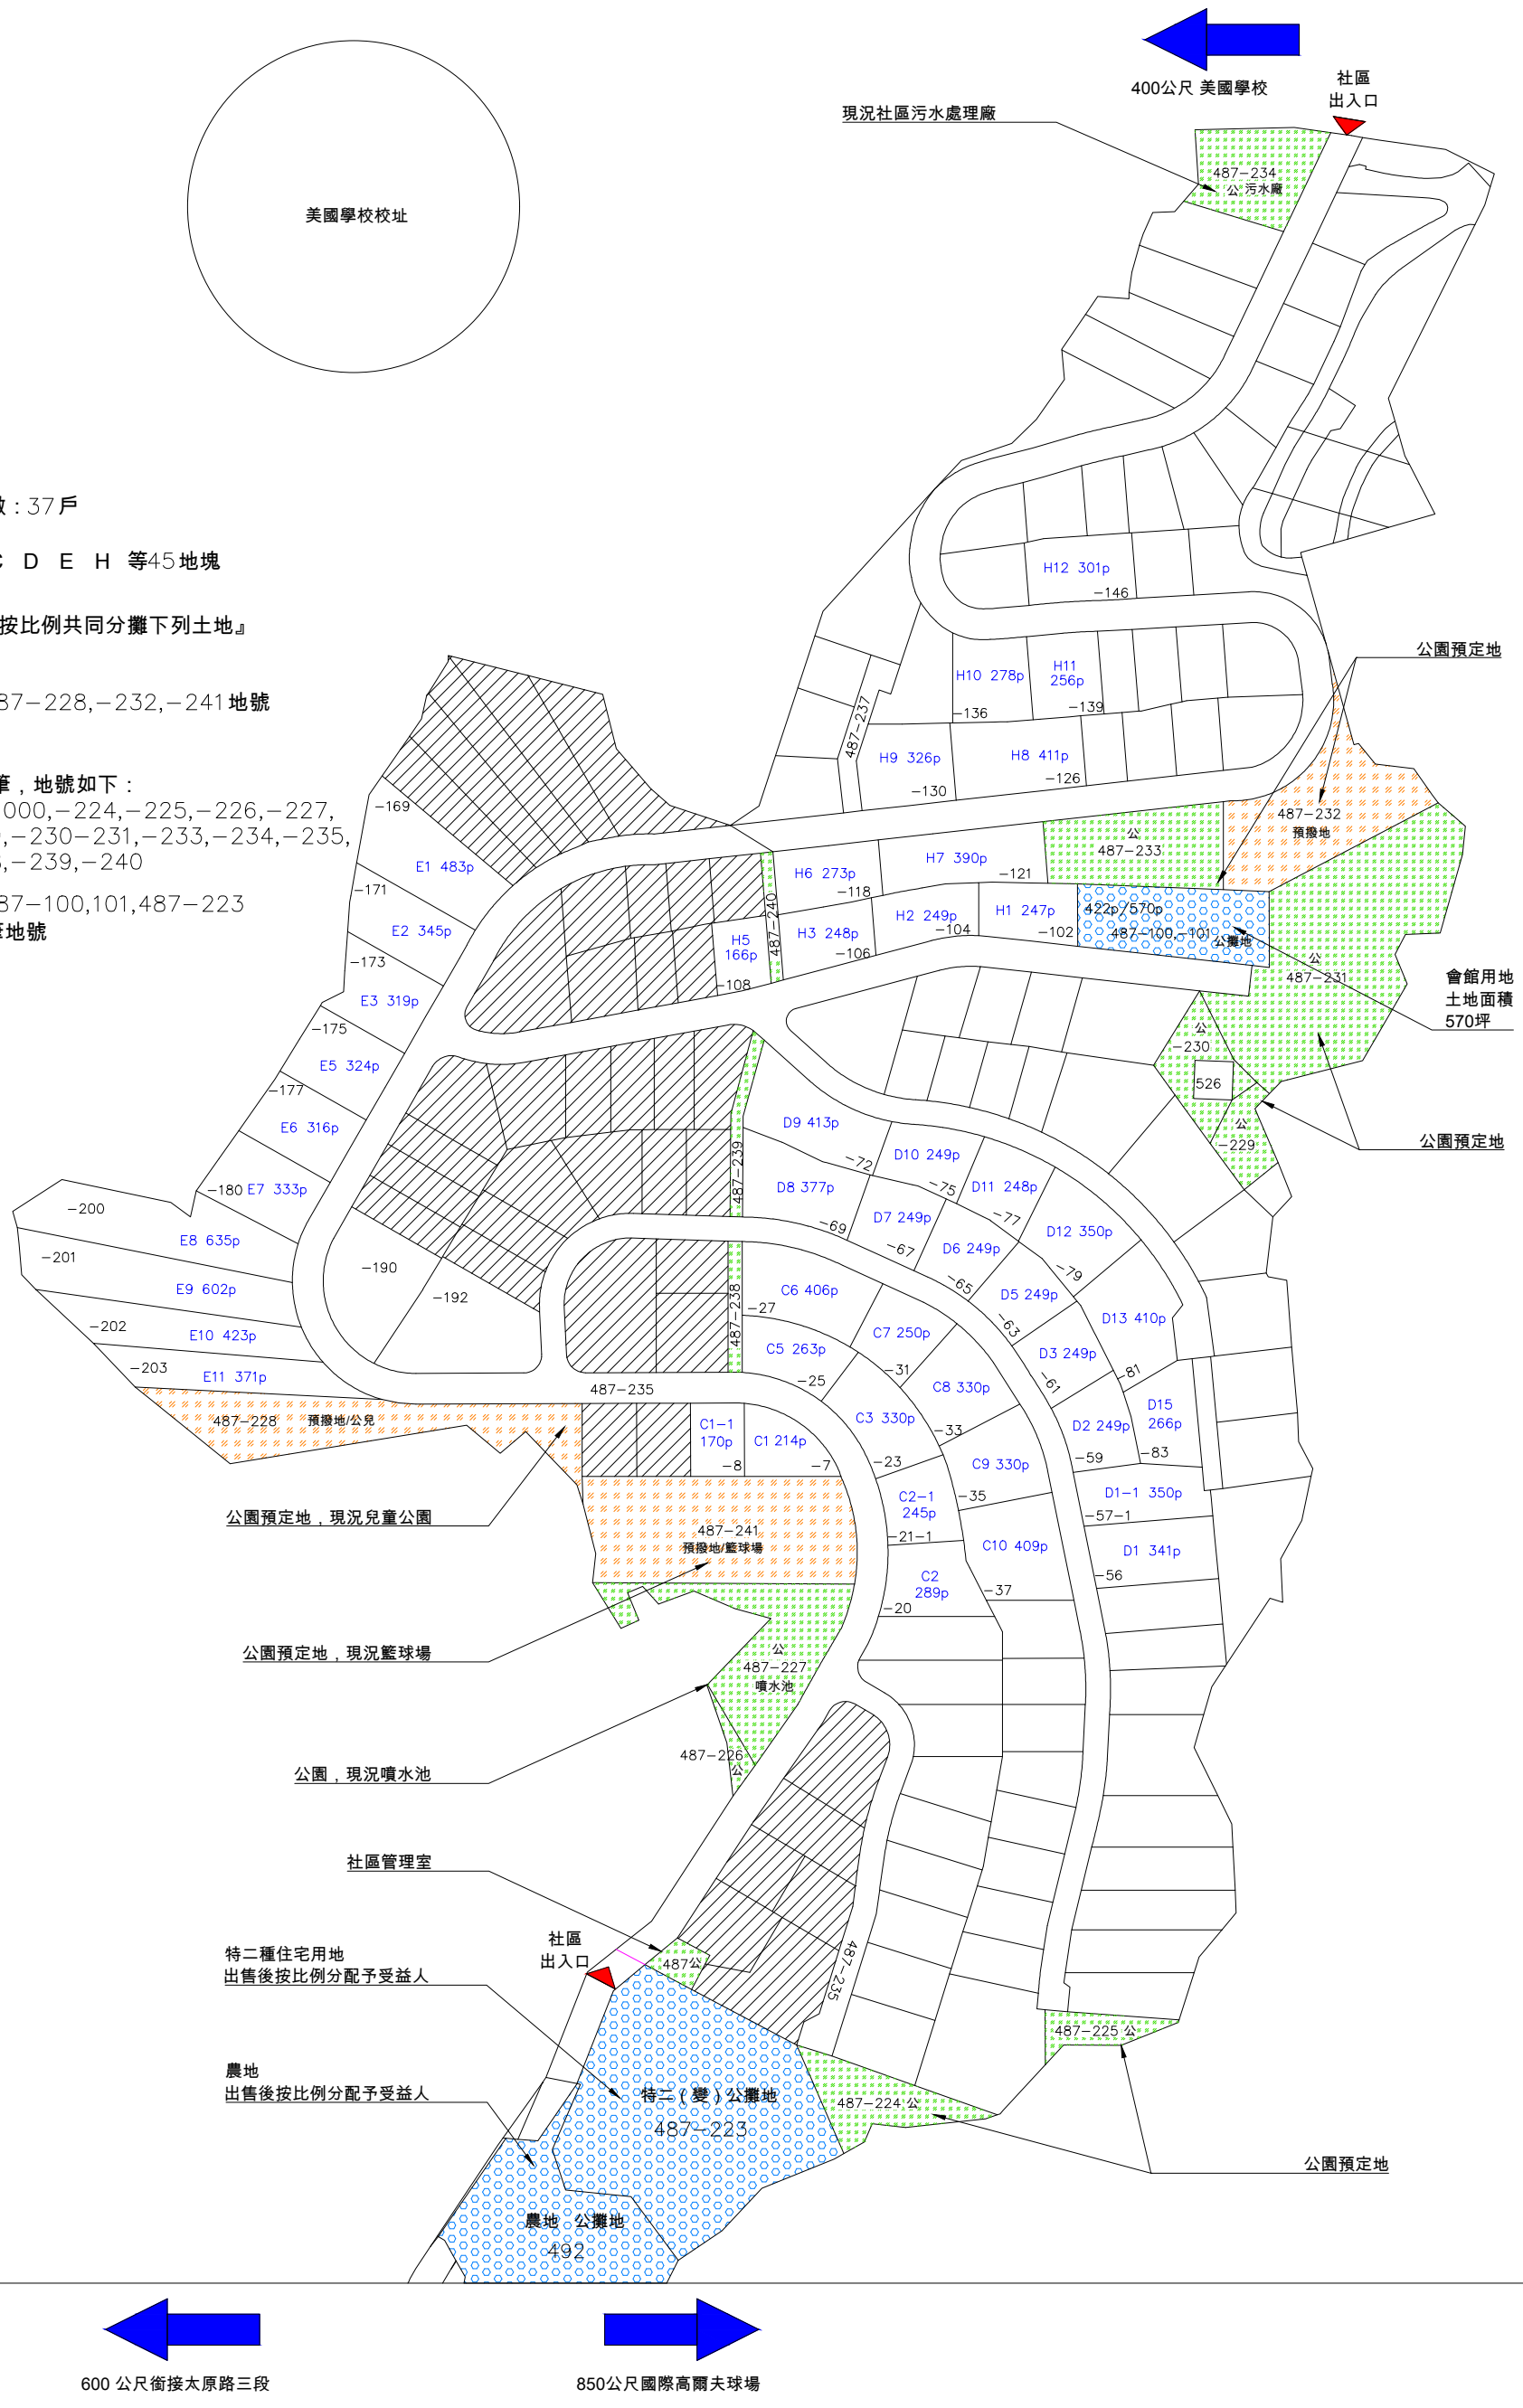
美國學校校址
400公尺 美國學校
社區
出入口
現況社區污水處理廠
487－234
公 污水廠
－已完工戶數：37戶
－整合區：C D E H 等45地塊
『各單元需應按比例共同分攤下列土地』
預撥地：487－228,－232,－241地號
公設地14筆，地號如下：
487－000,－224,－225,－226,－227,
－229,－230－231,－233,－234,－235,
－238,－239,－240
公攤地：487－100,101,487－223
及農地五筆地號
H12 301p
－146
H10 278p
－136
H11
256p
－139
H9 326p
－130
H8 411p
－126
487－237
公園預定地
487－232
預撥地
公
487－233
H7 390p
－121
H6 273p
－118
H2 249p
－104
H1 247p
－102
422p 570p
487－100、101
公攤地
H3 248p
－106
H5
166p
－108
487－240
公
487－231
會館用地
土地面積
570坪
公
－230
526
公
－229
公園預定地
－169
E1 483p
－171
E2 345p
－173
E3 319p
－175
E5 324p
－177
E6 316p
－180 E7 333p
－200
E8 635p
－201
E9 602p
－202
E10 423p
－203
E11 371p
－190
－192
487－239
D9 413p
－72
D10 249p
－75
D11 248p
－77
D8 377p
－69
D7 249p
－67
D6 249p
－65
D12 350p
－79
D5 249p
－63
D13 410p
D3 249p
－61
－81
D15
266p
－83
D2 249p
－59
D1－1 350p
－57－1
D1 341p
－56
487－238
－27
C6 406p
C5 263p
－25
C7 250p
－31
C8 330p
－33
C3 330p
－23
C9 330p
－35
C2－1
245p
－21－1
C10 409p
－37
C2
289p
－20
487－235
487－228
預撥地/公兒
C1－1
170p
－8
C1 214p
－7
公園預定地，現況兒童公園
487－241
預撥地/籃球場
公園預定地，現況籃球場
公
487－227
噴水池
487－226
公
公園，現況噴水池
社區管理室
社區
出入口
487公
特二種住宅用地
出售後按比例分配予受益人
487－235
487－225 公
農地
出售後按比例分配予受益人
特二（變）公攤地
487－223
487－224 公
公園預定地
農地 公攤地
492
600 公尺銜接太原路三段
850公尺國際高爾夫球場